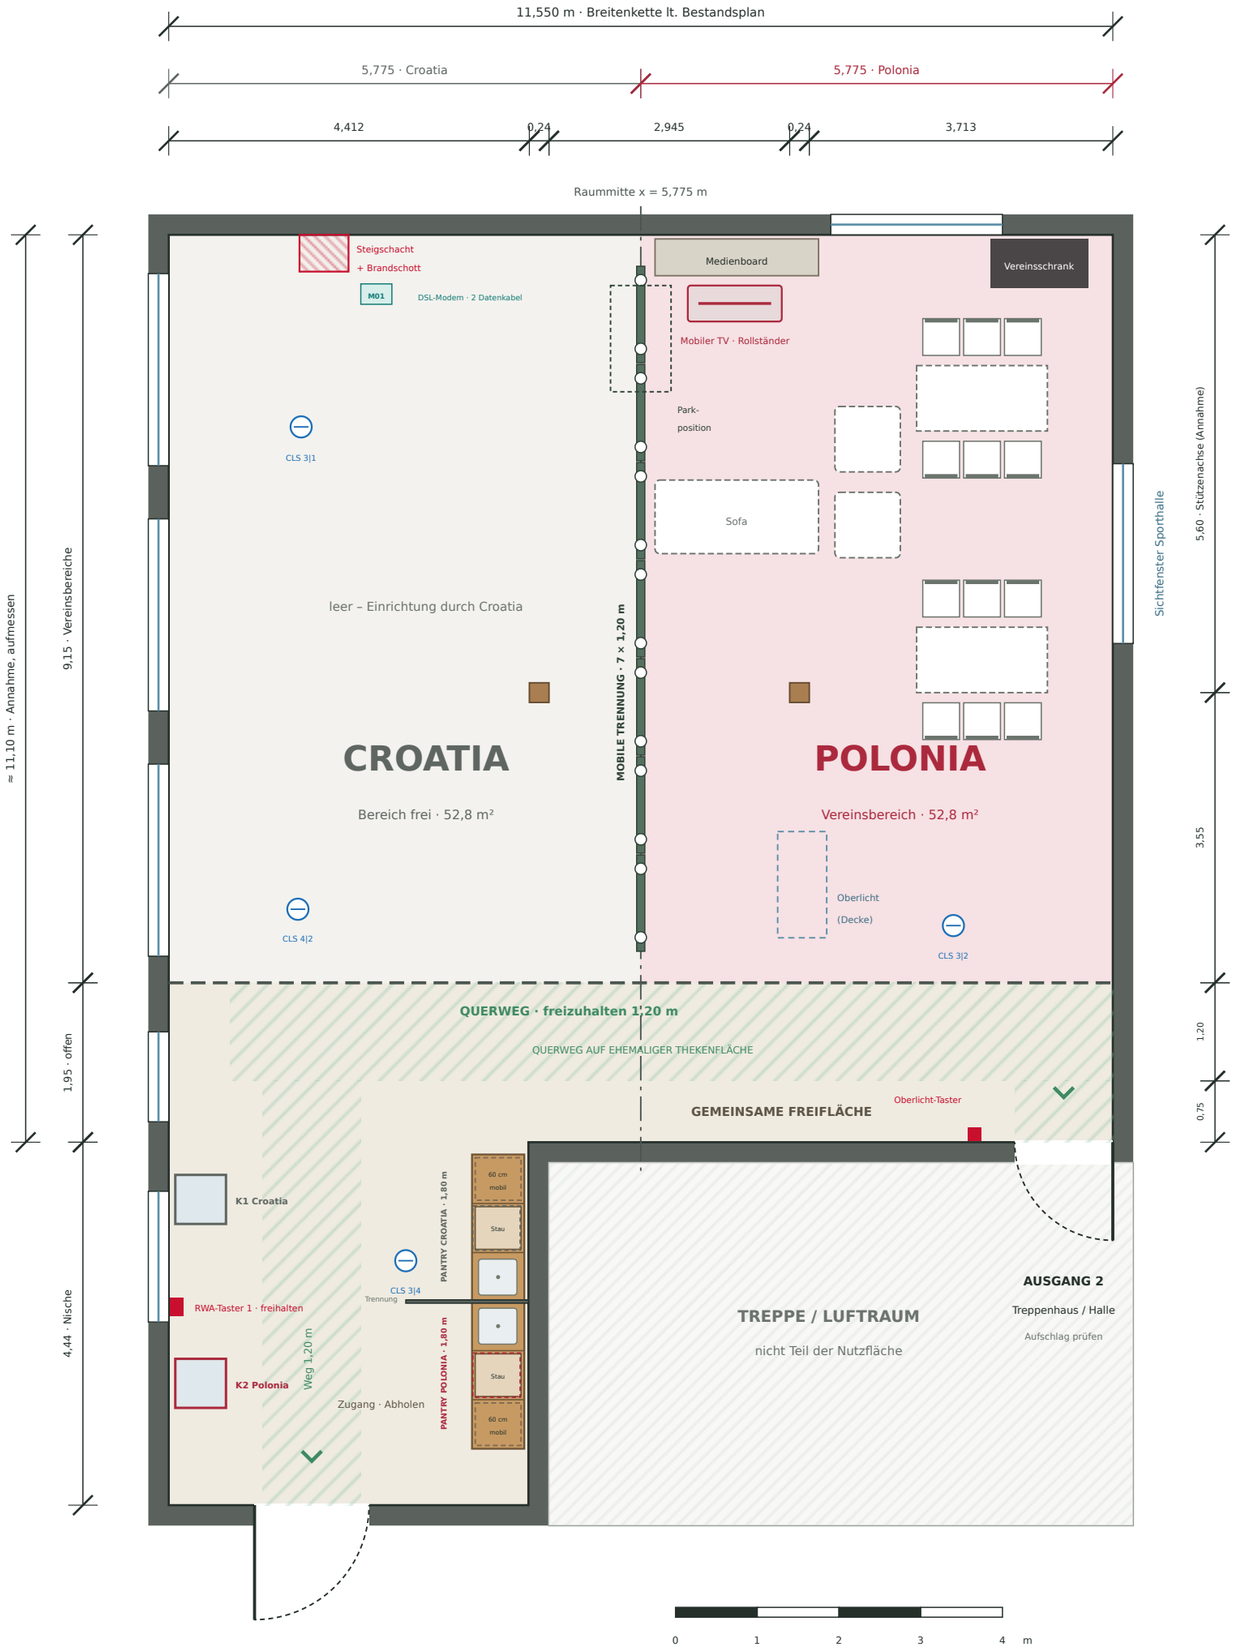


M 1:75 bei Druck auf A3 quer

KS POLONIA · CLUBRAUM 201

Alternative B: Drei Bereiche

Grundriss Bereichsaufteilung · Entwurf 05 · 13.11.2026

BEREICHE UND FLÄCHEN

Croatia-Bereich	5,775 × 9,15 m	**52,8 m²**
Polonia-Bereich	5,775 × 9,15 m	**52,8 m²**
Gemeinsamer Bereich	11,55 × 1,95 + Nische 4,40 × 4,44	**42,1 m²**
Summe (Plan: 147,79 m²)		**147,7 m²**

LEGENDE

- Mobile Trennung, Raster 1,20 m, auf Rollen, frei stehend
- Bereichsgrenze offen – keine Wand, nur Boden/Licht
- Verkehrs-/Fluchtweg freihalten, Planung 1,20 m
- Küchenzeile, Arbeitshöhe ca. 93 cm
- Möblierung nur beispielhaft (Nutzungsplanung folgt)
- Sicherheitsleuchte Bestand (CLS) – nicht verdecken
- Steigschacht / Taster Bestand – zugänglich halten
- Holzstütze 24/24 – keine Befestigung ohne Statik

KONZEPT

Teilung Exakt in Raummitte x = 5,775 m: beide Vereinsbereiche gleich groß (je 52,8 m²). Polonia: mobiler TV auf Rollständer, Medienboard, Vereinsschrank, Lounge, Tische.

Trennung 7 freistehende Elemente à 1,20 m, wahlweise Akustik-Stellwand (H ≤ 2,0 m) oder Pflanzkübel auf Rollen im gleichen Raster – auch gemischt. Für gemeinsame Events an der Nordwand zusammenschieben: ein großer, offener Raum.

Offen Richtung Freifläche keine Wand: beide Bereiche münden direkt in den Querweg und erreichen beide Ausgänge, ohne den anderen Bereich zu queren.

Querweg Die bisherige Thekenfläche wird Teil des 1,20 m breiten Querwegs. Der 1,20-m-Querweg und die Wege zu beiden Ausgängen bleiben frei.

Pantrys Zwei gleiche 1,80-m-Zeilen mit Spüle, Stauraum und je einem Hängeschrank. Je 60 cm freie Arbeitsplatte für ein zeitweise genutztes mobiles Induktionsfeld. Wasser/Abwasser, Strom und Geräteabstände vor Ausführung prüfen; K1/K2 separat.

Daten M01 neben dem Steigschacht; D01 nach Polonia, D02 zum AP bei K1/K2.

VOR UMSETZUNG PRÜFEN

- Aufmaß: Raumtiefe 11,10 m und Stützenachse 5,60 m sind Annahmen; neue Bereichsgrenze 9,15 m und freie Wege vor Ort prüfen.
- Brandschutz: mobile Trennung darf Rauchmelder, RWA, Sicherheitsbeleuchtung und Fluchtwege nicht beeinträchtigen – Höhe/Material mit Brandschutz klären.
- Trennelemente standsicher (Fuß/Bremse), nicht an Holzstützen/Dach befestigen.
- Pflanzen: Gewicht/Bewässerung auf Estrich, schwer entflammbare Kübel.
- Tür Treppenhaus/Halle: Aufschlagrichtung und Lage vor Ort bestätigen.
- Zweite Spüle: Wasser/Abwasser, Steckdosen und Kochfeld-Abstände prüfen.
- Nutzung beider Vereine (Schlüssel, Kosten, Zeiten) vertraglich regeln.

BASIS

Bestandsplan Raum 201 Clubraum: F 147,79 m², lichte Höhe 4,75 m, Estrich, Trapezblech.
Skizze Bereichsaufteilung vom 01.11.2026; Geometrie wie Konzept v11 (room.json).
Konzeptplanung – keine Ausführungs-, Brandschutz- oder Genehmigungsplanung.
Nächste Schritte: Aufmaß, Wegeprüfung und Nutzungsplanung je Bereich.

KS Polonia Hamburg e.V. 1988 · Clubraum 201 · Alternative B	
Plan: Grundriss Bereiche	**Status: KONZEPT / Entwurf**
Maßstab 1:75 (A3) · Maße in m	Alle Maße vor Ort prüfen
Planstand B-05 · 13.11.2026	Ursprung: linke obere Innenecke