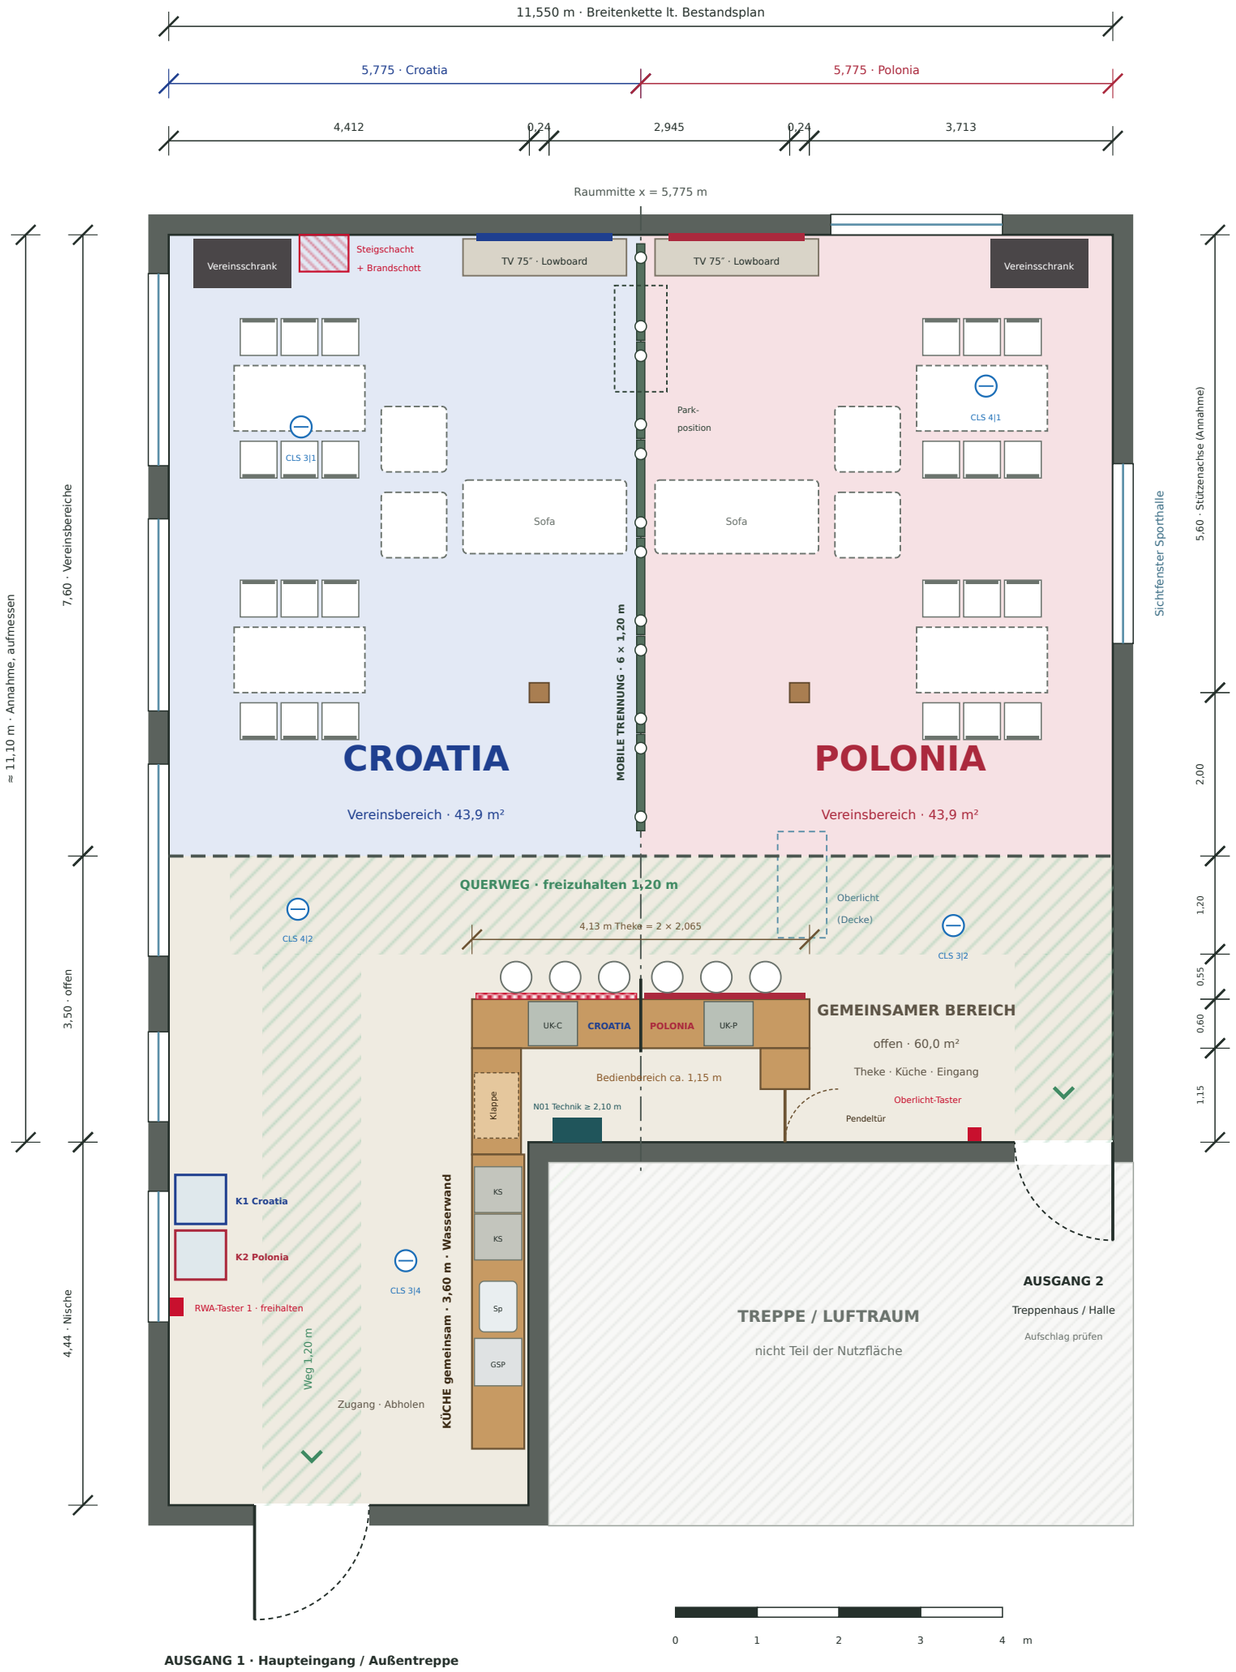


M 1:75 bei Druck auf A3 quer

KS POLONIA · CLUBRAUM 201

Alternative B: Drei Bereiche

Grundriss Bereichsaufteilung · Entwurf 01 · 01.11.2026

BEREICHE UND FLÄCHEN

Croatia-Bereich	5,775 × 7,60 m	**43,9 m²**
Polonia-Bereich	5,775 × 7,60 m	**43,9 m²**
Gemeinsamer Bereich	11,55 × 3,50 + Nische 4,40 × 4,44	**60,0 m²**
Summe (Plan: 147,79 m²)		**147,7 m²**

LEGENDE

- Mobile Trennung, Raster 1,20 m, auf Rollen, frei stehend
- Bereichsgrenze offen – keine Wand, nur Boden/Licht
- Verkehrs-/Fluchtweg freihalten, Planung 1,20 m
- Theke / Küchenzeile, Arbeitshöhe ca. 93 cm
- Möblierung nur beispielhaft (Nutzungsplanung folgt)
- Sicherheitsleuchte Bestand (CLS) – nicht verdecken
- Steigschacht / Taster Bestand – zugänglich halten
- Holzstütze 24/24 – keine Befestigung ohne Statik

KONZEPT

Teilung Exakt in Raummitte x = 5,775 m: beide Vereinsbereiche gleich groß (je 43,9 m²), jeweils mit eigenem TV, Lowboard, Vereinsschrank und eigener Sicherheitsleuchte.

Trennung 6 freistehende Elemente à 1,20 m, wahlweise Akustik-Stellwand (H ≤ 2,0 m) oder Pflanzkübel auf Rollen im gleichen Raster – auch gemischt. Für gemeinsame Events an der Nordwand zusammenschieben: ein großer Raum, beide TVs sichtbar.

Offen Richtung Theke keine Wand: beide Bereiche münden direkt in den Querweg und erreichen beide Ausgänge, ohne den anderen Bereich zu queren.

Theke Ein Korpus, zwei gleich lange Hälften (je 2,065 m, 3 Hocker): eigene Front, eigener Untertheken-Kühlschrank (UK-C / UK-P), eigene Kasse/Abrechnung. Zugang Croatia-Seite über Klappe zur Küche, Polonia-Seite über Pendeltür.

Küche Gemeinsam an der Wasserwand (unverändert); Getränke getrennt in K1 / K2.

Technik N01 Netzwerk in den gemeinsamen Bereich verlegt; Steigschacht frei.

VOR UMSETZUNG PRÜFEN

- Aufmaß: Raumtiefe 11,10 m, Stützenachse 5,60 m und Bereichsgrenze 7,60 m sind aus Plan/Skizze abgeleitet – Theke erst nach Aufmaß bestellen.
- Brandschutz: mobile Trennung darf Rauchmelder, RWA, Sicherheitsbeleuchtung und Fluchtwege nicht beeinträchtigen – Höhe/Material mit Brandschutz klären.
- Trennelemente standsicher (Fuß/Bremse), nicht an Holzstützen/Dach befestigen.
- Pflanzen: Gewicht/Bewässerung auf Estrich, schwer entflammbare Kübel.
- Tür Treppenhaus/Halle: Aufschlagrichtung und Lage vor Ort bestätigen.
- Nutzung beider Vereine (Schlüssel, Kosten, Zeiten) vertraglich regeln.

BASIS

Bestandsplan Raum 201 Clubraum: F 147,79 m², lichte Höhe 4,75 m, Estrich, Trapezblech.
Skizze Bereichsaufteilung vom 01.11.2026; Geometrie wie Konzept v11 (room.json).
Konzeptplanung – keine Ausführungs-, Brandschutz- oder Genehmigungsplanung.
Nächste Schritte: Visualisierung 3D, Nutzungs- und Möblierungsplanung je Bereich.

KS Polonia Hamburg e.V. 1988 · Clubraum 201 · Alternative B	
Plan: Grundriss Bereiche	**Status: KONZEPT / Entwurf**
Maßstab 1:75 (A3) · Maße in m	Alle Maße vor Ort prüfen
Planstand B-01 · 01.11.2026	Ursprung: linke obere Innenecke